PHASE-1

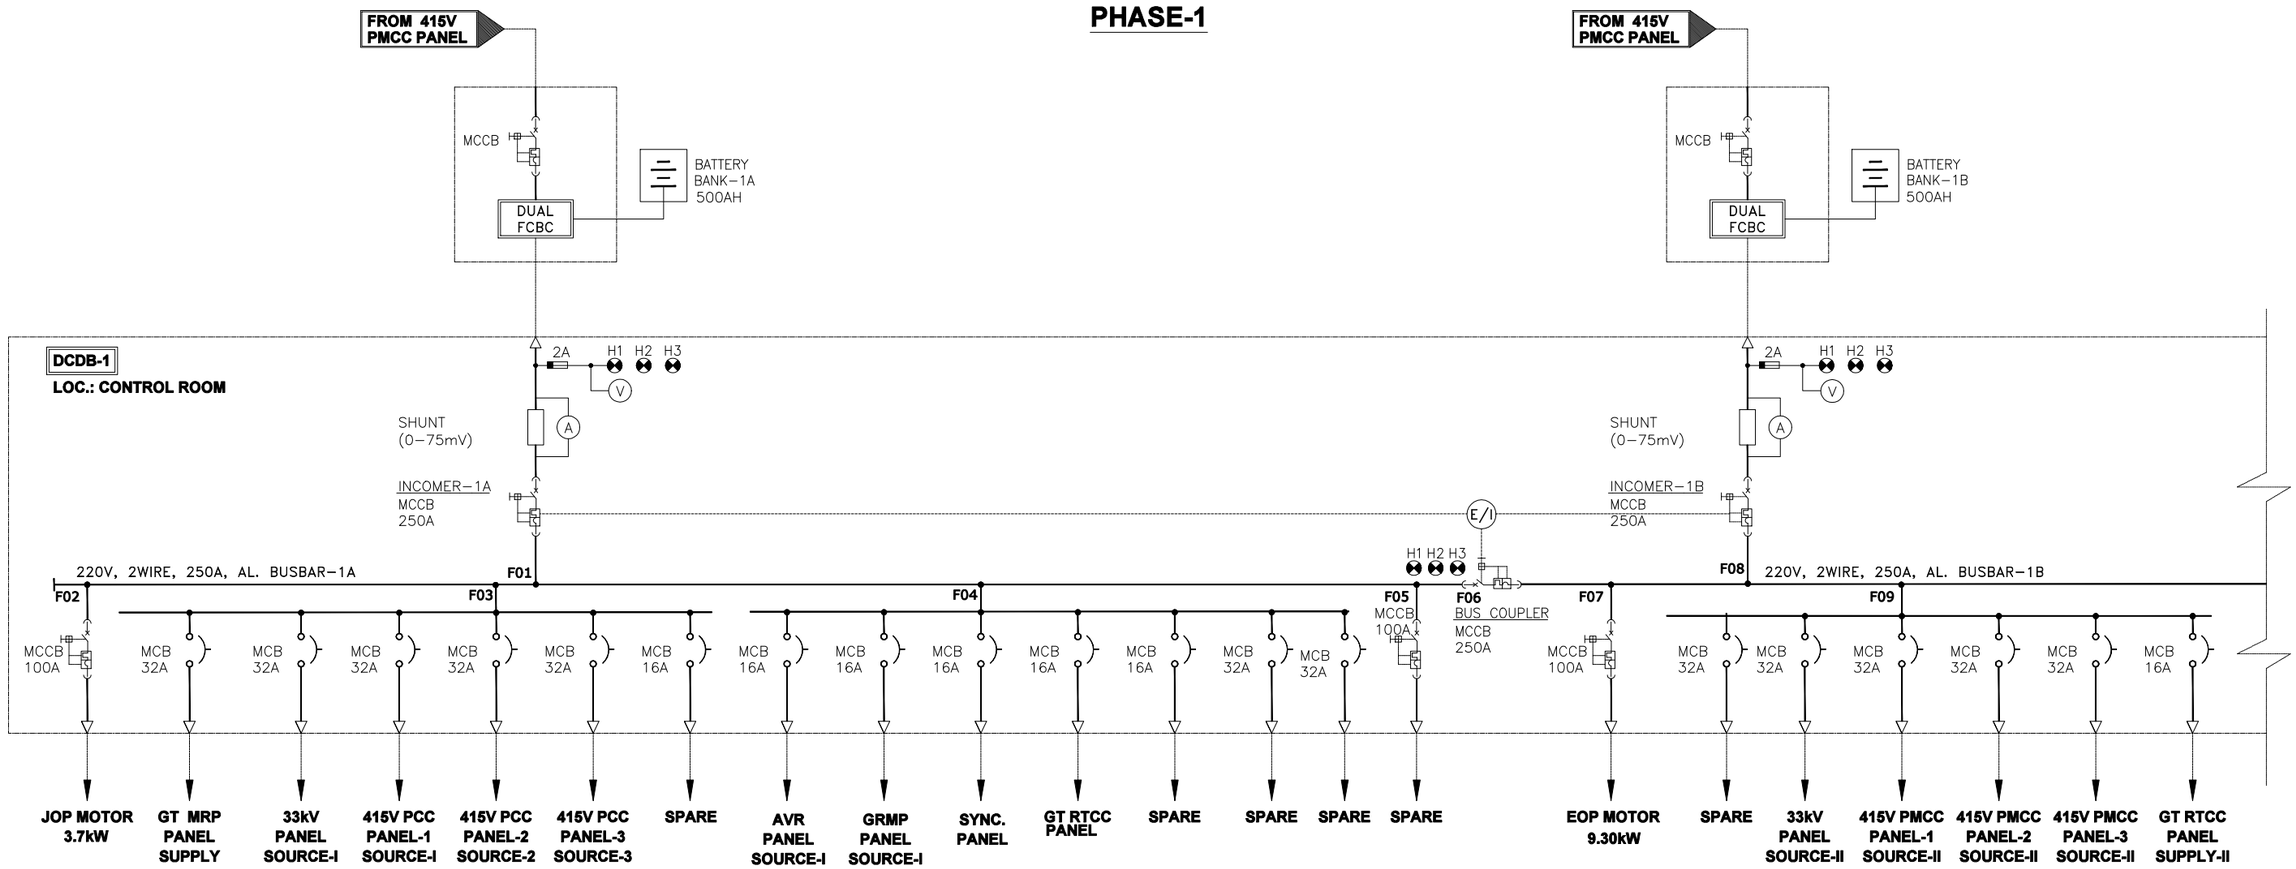

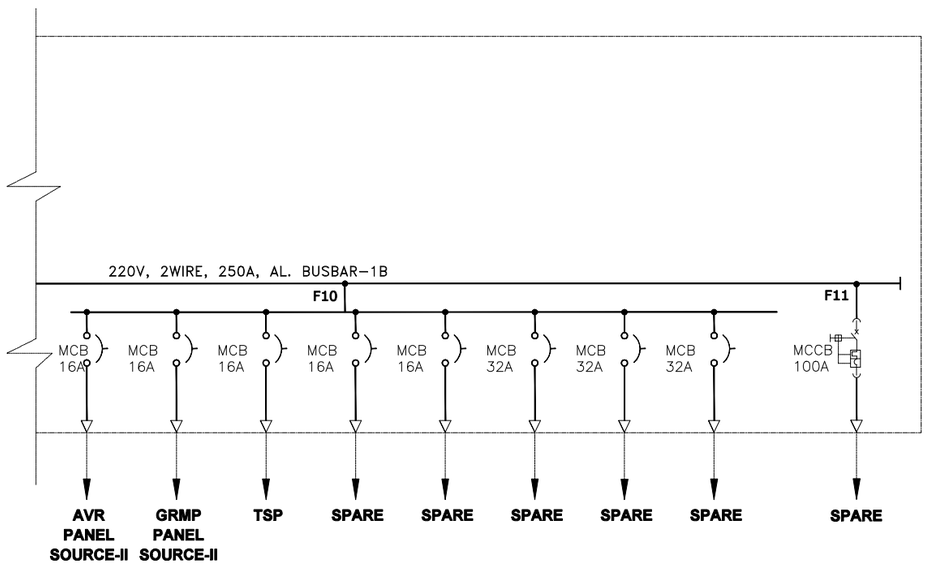

LEGENDS:-

SYMBOLS	DESCRIPTION
	MOLDED CASE CIRCUIT BREAKER
	MINIATURE CIRCUIT BREAKER
	FUSE
	CABLE TERMINATION
E/I	ELECTRICAL INTERLOCK
	EARTH
	BATTERY

METERING:-

SYMBOLS	DESCRIPTION
V	VOLTMETER
A	AMMETER

INDICATIONS:-

1. H1 – BREAKER ON (RED)
2. H2 – BREAKER OFF (GREEN)
3. H3 – BREAKER TRIP (AMBER)

PURPOSE OF ISSUE: TENDER ☐ INFORMATION ☐ REVIEW/APPROVAL ☑ CONSTRUCTION ☐ AS-BUILT ☐

PROJECT : 1X45MW CAPTIVE POWER PLANT,(PHASE-1) AT JAMSHEDPUR, JHARKHAND

CLIENT : M/S. GAJANAN FERRO PVT LTD.

THIS DRAWING IS THE PROPERTY OF M/s AQUATHERM ENGINEERING CONSULTANTS (INDIA) PVT. LTD. AND MUST NOT BE COPIED IN WHOLE OR PART OR LENTOUT WITHOUT THEIR WRITTEN PERMISSION.

	NAME	SIGN	DATE
DRN.	V.R.I	V.R.I	01.07.25
CHKD.	S.P	S.P	01.07.25
APPD.	R.A	RA	01.07.25

AQUATHERM
ENGINEERING CONSULTANTS (INDIA) PVT. LTD.
CHENNAI, TAMILNADU - 600 004 : INDIA

UNLESS OTHERWISE STATED ALL DIMENSIONS ARE IN mm

SCALE	CAD FILE	SIZE
1:1	–	A3

TITLE: DC DISTRIBUTION SLD

DRAWING NO. 3-11894-400-005 REV. 0

SHEET NO. 01 NO. OF SHT. 01

REV	DATE	DESCRIPTION	DRN.	CHKD.	APPD.
0	01.07.25	FIRST ISSUE	V.R.I	S.P	R.A

REVISIONS